Système de gestion des décisions des instances
RECOMMANDATION

CA : 40.01

2024/06/03
19:00

Dossier # : 1246880006

Unité administrative responsable :	Arrondissement Côte-des-Neiges - Notre-Dame-de-Grâce , Direction des travaux publics , Division des études techniques
Niveau décisionnel proposé :	Conseil d'arrondissement
Charte montréalaise des droits et responsabilités :	Art. 24 d) favoriser les modes de transport collectif et actif ainsi que les autres modes de transport ayant pour effet de limiter l'usage de la voiture en milieu urbain en vue de réduire la pollution atmosphérique et les émissions de gaz à effet de serre
Compétence d'agglomération :	Réseau cyclable identifié au Plan de transport
Projet :	Plan de transport
Objet :	Édicter une ordonnance relative à la mise à sens unique de la rue de Terrebonne en vue d'ajouter un aménagement cyclable protégé entre les avenues Saint-Ignatius et l'avenue Girouard.

Il est recommandé :
D'édicter une ordonnance relative à la mise à sens unique de la rue de Terrebonne en vue d'ajouter un aménagement cyclable protégé entre les avenues Saint-Ignatius et l'avenue Girouard.

Signé par Stephane P PLANTE **Le** 2024-05-30 13:56

Signataire : Stephane P PLANTE

_____

Directeur d'arrondissement
Côte-des-Neiges - Notre-Dame-de-Grâce , Bureau du directeur d'arrondissement

Montréal

Système de gestion des décisions des instances
SOMMAIRE DÉCISIONNEL

IDENTIFICATION **Dossier # :1246880006**

Unité administrative responsable :	Arrondissement Côte-des-Neiges - Notre-Dame-de-Grâce , Direction des travaux publics , Division des études techniques
Niveau décisionnel proposé :	Conseil d'arrondissement
Charte montréalaise des droits et responsabilités :	Art. 24 d) favoriser les modes de transport collectif et actif ainsi que les autres modes de transport ayant pour effet de limiter l'usage de la voiture en milieu urbain en vue de réduire la pollution atmosphérique et les émissions de gaz à effet de serre
Compétence d'agglomération :	Réseau cyclable identifié au Plan de transport
Projet :	Plan de transport
Objet :	Édicter une ordonnance relative à la mise à sens unique de la rue de Terrebonne en vue d'ajouter un aménagement cyclable protégé entre les avenues Saint-Ignatius et l'avenue Girouard.

CONTENU

CONTEXTE

L'arrondissement de Côte-des-Neiges - Notre-Dame-de-Grâce (CDN-NDG) possède l'expertise et la compétence technique pour superviser les études, la conception et la réalisation d'aménagements cyclables. Par conséquent, nous avons offert au Service de l'urbanisme et de la mobilité, la prise en charge des études, la conception et la réalisation d'un aménagement cyclable rehaussé sur la rue de Terrebonne, en vertu de l'article 85 alinéa 2 de la Charte de la Ville de Montréal, ce qui a été accepté par le SUM (CA24 170018).

Pour 2024, l'Arrondissement souhaite rehausser l'aménagement cyclable sur la rue de Terrebonne sur une longueur de 2,5 km entre l'avenue Saint-Ignatius et l'avenue Girouard. Actuellement, l'aménagement cyclable présent sur cette rue se limite à une chaussée désignée et la circulation véhiculaire est permise dans les 2 directions avec 1 bande de stationnement de chaque côté.

Après avoir fait une étude de circulation exhaustive avec une firme externe afin de déterminer l'aménagement cyclable optimal pour les besoins du secteur, l'arrondissement souhaite réaliser le scénario retenu dans cette étude. L'aménagement proposé est constitué de bandes cyclables unidirectionnelles protégées sur toute la longueur, d'un côté par des bollards et de l'autre par la bande de stationnement restante et la circulation véhiculaire sera à sens unique. Entre l'avenue Coronation et le boulevard Cavendish, le sens unique sera en direction ouest et entre le boulevard Cavendish et l'avenue Girouard, le sens unique sera en direction est. La circulation à double sens sera conservée entre les avenues Saint-Ignatius et Coronation afin de maintenir l'accès au campus Loyola et de maintenir un patron de circulation cohérent dans le secteur. La mise à sens unique est un élément essentiel au

projet afin de redonner cet espace aux aménagements cyclables protégés.

Outre les avantages pour les cyclistes, cette mise à sens unique permettra de limiter la circulation véhiculaire sur cet axe, réduisant les conflits possibles entre les véhicules motorisés et les usagers du transport actifs, ce qui est souhaitable étant donné la présence de plusieurs écoles et parcs le long de cet axe. Il est également à noter que le projet prévoit l'ajout de signalisation permettant de renforcer les interdictions de stationner à moins de 5 mètres des intersections, afin d'améliorer la visibilité et la sécurité de l'ensemble des usagers de cette rue.

Le projet comprend également des ajustements aux plans de feux de circulation (PE) aux intersections suivantes :

-08 Terrebonne/Cavendish
-24 Terrebonne/Grand
-20 Terrebonne/Draper
-118 Terrebonne/Girouard

L'aménagement cyclable sera de type ‘’transitoire’’ et n’impliquera aucun travail de voirie. Les travaux sont composés principalement de changements de marquage, de signalisation et d'ajout de bollards. L’Arrondissement souhaite déployer tôt durant la période estivale de 2024, soit vers la fin du mois de juin, une fois la période scolaire terminé.

Recommandation

Pour faire suite à l'étude du dossier, il est recommandé :

- D'enlever la signalisation de chaussée désignée en direction ouest entre l'avenue Saint-Ignatius et l'avenue Girouard;
- D'enlever la signalisation de chaussée désignée en direction est entre l'avenue Saint-Ignatius et l'avenue Girouard;
- De mettre la rue de Terrebonne à sens unique vers l'ouest, excepté vélo entre l'avenue Coronation et le boulevard Cavendish;
- De mettre la rue de Terrebonne à sens unique vers l'est, excepté vélo entre le boulevard Cavendish et l'avenue Old Orchard;
- D'ajouter une bande cyclable unidirectionnelle vers l'ouest du côté nord de la rue de Terrebonne entre l'avenue Saint-Ignatius et l'avenue Girouard;
- D'ajouter une bande cyclable unidirectionnelle vers l'est du côté sud de la rue de Terrebonne entre l'avenue Saint-Ignatius et l'avenue Girouard;

- D'ajouter un arrêt à l'approche est de l'intersection de l'avenue Belmore (nord) et de la rue de Terrebonne;
- D'ajouter une obligation de tout droit et virage à droite pour l'approche sud de l'intersection du boulevard Grand et de la rue de Terrebonne;
- D'ajouter une obligation de tout droit et virage à gauche pour l'approche nord de l'intersection du boulevard Grand et de la rue de Terrebonne;
- D'ajouter une obligation de tout droit et virage à gauche pour l'approche nord de l'intersection de l'avenue Draper et de la rue de Terrebonne;
- D'ajouter une prescription de virage à gauche pour la voie de gauche à l'approche ouest de l'intersection de l'avenue Girouard et la rue de Terrebonne;
- D'ajouter une prescription de tout droit et de virage à droite pour la voie de droite à l'approche ouest de l'intersection de l'avenue Girouard et la rue de Terrebonne;

- D'ajouter une zone d'arrêt interdit sur le côté nord de la rue de Terrebonne, entre l'avenue Saint-Ignatius et l'avenue Madison;
- D'ajouter une zone d'arrêt interdit sur le côté sud de la rue de Terrebonne, entre

l'avenue Saint-Ignatius et l'avenue Coronation;
- D'ajouter une zone d'arrêt interdit sur le côté sud de la rue de Terrebonne, entre l'avenue Madison et l'avenue Royal;
- D'ajouter une zone d'arrêt interdit sur le côté nord de la rue de Terrebonne, entre l'avenue Royal et l'avenue Draper;
- D'ajouter une zone d'arrêt interdit sur le côté sud de la rue de Terrebonne, entre l'avenue Draper et l'avenue Girouard;
- D'enlever une zone de stationnement 15 minutes de 7 h à 9 h et de 14 h à 16 h du lundi au vendredi de septembre à juin sur le côté nord de la rue de Terrebonne, 38 mètres à l'est de l'avenue Benny, sur une distance d'environ 30 mètres;
- D'ajouter une zone de stationnement 15 minutes de 7h à 9h et de 14h à 16h du lundi au vendredi de septembre à juin sur le côté sud de la rue de Terrebonne, 8 mètres à l'est de l'avenue Benny, sur une distance d'environ 30 mètres;
- D'enlever une zone de stationnement pour personne à mobilité réduite sur le côté sud de la rue de Terrebonne, 3 mètres à l'ouest de l'avenue Benny, sur une distance d'environ 6 mètres;
- D'ajouter une zone de stationnement pour personne à mobilité réduite sur le côté est de l'avenue Benny, 8 mètres à sud de la rue de Terrebonne, sur une distance d'environ 6 mètres;
- Conserver toute autre réglementation en vigueur.

DÉCISION(S) ANTÉRIEURE(S)

CA24 170018 Adopter une résolution visant à offrir au conseil municipal, la prise en charge de la conception et de la réalisation des travaux pour un aménagement cyclable rehaussé sur la rue de Terrebonne, en vertu de l'article 85 alinéa 2 de la Charte de la Ville de Montréal.

CG23 0749 Adopter une résolution visant à maintenir, jusqu'au 31 décembre 2024, la délégation du conseil d'agglomération au conseil de la ville de certains pouvoirs concernant les équipements, infrastructures et activités d'intérêt collectif mentionnés en annexe du Décret concernant l'agglomération de Montréal (1229-2005, 8 décembre 2005).

CM23 1465 Adopter une résolution visant à accepter, jusqu'au 31 décembre 2024, la délégation au conseil de la ville de certains pouvoirs concernant les équipements, infrastructures et activités d'intérêt collectif mentionnés en annexe du Décret concernant l'agglomération de Montréal (1229-2005, 8 décembre 2005).

DESCRIPTION

- Le nombre de kilomètres de voie cyclable protégée ajoutés au réseau; **2,5 km**
- Le nombre de kilomètres de voie cyclable non protégée ajoutés au réseau; **0**
- Le nombre de SAS vélo ajouté au réseau; **2**
- Le nombre de kilomètres de rues réaménagés; **N/A**
- Le nombre d'intersections sécurisées/réaménagées; **N/A**
- Le nombre de m2 nouvellement verdis ou déminéralisés; **N/A**
- Le nombre d'arbres ajoutés. **N/A**

JUSTIFICATION

Ces opportunités de développement permettront de répondre à la demande d'un nombre croissant de cyclistes, de faire le lien avec les aménagements cyclables existants, d'assurer la visibilité des cyclistes par les autres usagers et enfin, d'améliorer la sécurité et le

sentiment de confort pour les cyclistes de tous âges. En effet, plusieurs personnes incluant les familles avec enfants en période d'apprentissage ou encore des personnes de l'âge d'or ne pratiquent pas le vélo sur les rues de la métropole parce qu'elles ne se sentent pas en sécurité. Ces aménagements devraient donc contribuer à un transfert modal en faveur du transport actif, ce qui favorisera l'adoption de saines habitudes de vie en termes de santé et d'activité physique et aussi contribuer à la lutte aux changements climatiques.

ASPECT(S) FINANCIER(S)

La valeur estimée des coûts du projet est de 250 000 $.

Ce sont essentiellement des travaux de signalisation, d'installation de bollards, de marquage et de modification des feux de circulation.

Les coûts reliés aux travaux de rehaussement des aménagements cyclables sont assumés par le budget de fonctionnement du Service de l'urbanisme et de la mobilité (SUM).

MONTRÉAL 2030

Ce dossier contribue à l'atteinte du plan stratégique 2023-2030 de l'arrondissement en :

- Offrant des milieux de vie sains et durables (axe 2 du plan), en permettant à la population de se déplacer de façon plus active grâce à des aménagements accessibles et sécuritaires. (résultat 2.2 du plan).

Ces travaux permettront également de contribuer à l'atteinte des objectifs suivants :

- Améliorer la sécurité des clientèles vulnérables (piétons, écoliers et personnes à mobilité réduite);
- Apaiser la circulation.

IMPACT(S) MAJEUR(S)

La réalisation d'aménagements cyclables prévus dans le cadre du présent sommaire a un impact majeur sur la sécurité des cyclistes en minimisant les risques d'accident. Cela encourage aussi plus de résidents de l'Arrondissement à utiliser le vélo comme mode de transport, avec les nombreux bénéfices individuels et collectifs que cela implique. La mise à sens unique amènera des changements par rapport aux parcours véhiculaires dans le secteur.

OPÉRATION(S) DE COMMUNICATION

Le projet d'aménagement cyclable sur la rue de Terrebonne a été annoncé officiellement via un communiqué de presse le 30 octobre 2023. Une séance d'information citoyenne a aussi été faite le 30 novembre 2023. Des avis de travaux seront distribués dans le secteur et des affiches seront installées sur la rue de Terrebonne quelques semaines avant le début des travaux afin d'informer la population sur le projet et sur les dates des différentes phases d'implantation.

CALENDRIER ET ÉTAPE(S) SUBSÉQUENTE(S)

3 juin 2024 : Résolution du conseil d'arrondissement pour les changements de signalisation des aménagements cyclables 2024.
fin Juin 2024 : Réalisation sur le terrain des changements de signalisation.

CONFORMITÉ AUX POLITIQUES, AUX RÈGLEMENTS ET AUX ENCADREMENTS ADMINISTRATIFS

Le signataire de la recommandation atteste de la conformité aux politiques, règlements et aux encadrements administratifs.

VALIDATION

Intervenant et sens de l'intervention

Autre intervenant et sens de l'intervention

Parties prenantes

Damien LE HENANFF, Service de l'urbanisme et de la mobilité
Raynald MACHER-POITRAS, Service de l'urbanisme et de la mobilité

Lecture :

Raynald MACHER-POITRAS, 27 mai 2024

RESPONSABLE DU DOSSIER

Jonathan J LEDUC
Conseiller en aménagement

Tél : 514-234-7907
Télécop. : 514-872-0918

ENDOSSÉ PAR Le : 2024-05-14

Pascal TROTTIER
chef(fe) de division - etudes techniques en arrondissement

Tél : 514-206-0495
Télécop. :

Système de gestion des décisions des instances
PIÈCES JOINTES AU DOSSIER

Dossier # : 1246880006

Unité administrative responsable :	Arrondissement Côte-des-Neiges - Notre-Dame-de-Grâce , Direction des travaux publics , Division des études techniques
Objet :	Édicter une ordonnance relative à la mise à sens unique de la rue de Terrebonne en vue d'ajouter un aménagement cyclable protégé entre les avenues Saint-Ignatius et l'avenue Girouard.



20240116_Lettre_Résultats_AP2_2024_CDNNDG_HB.pdf



F2301135_L06_04@05_v4.pdf



F2301135_L06_06@07_v5.pdf

RESPONSABLE DU DOSSIER

Jonathan J LEDUC
Conseiller en aménagement

Tél : 514-234-7907
Télécop. : 514-872-0918

Urbanisme et mobilité
Montréal

Direction des projets d'aménagement urbain
Bureau du directeur
801, rue Brennan, 6e étage
Montréal (Québec) H3C 0G4

PAR COURRIEL

Le 16 janvier 2024

Monsieur Stéphane Plante
Directeur
Arrondissement Côte-Des-Neiges-Notre-Dame-De-Grâce
5160, boul. Décarie, suite 600
Montréal (Québec) H3X 2H9
stephane.plante@montreal.ca

Objet : Résultats - Appel à projets 2023-2024

Monsieur,

Dans le cadre de l'appel à projets réalisé par le Service de l'urbanisme et de la mobilité en 2023, j'ai le plaisir de vous annoncer les projets soumis par votre arrondissement qui ont été sélectionnés pour une réalisation d'ici la fin de l'année 2024.

Le tableau ci-dessous détaille les projets sélectionnés ainsi que le financement accordé, en fonction des budgets estimés qui nous ont été présentés par vos équipes :

Numéro de projet	Titre du projet	Financement PTI-45000	Financement PTI-59070	Financement BF Vélo	Financement Vision Zero
SUM_CDN24-0801	Réaménagement de la Promenade Jean-Brillant				2 923 576 $
SUM_CDN24-0802	Installation d'une clôture sur le terre-plein central de Cavendish entre la rue Sherbrooke Ouest et le viaduc de la rue Maisonneuve Ouest		495 000 $		
SUM_CDN24-0907	Aménagement cyclable rehaussé sur la rue Terrebonne			220 000 $	

En contrepartie, nous vous informons que les projets suivants n'ont pu être sélectionnés dans le cadre du processus de l'appel à projets. Le tableau ci-dessous détaille les projets non-sélectionnés ainsi que les motifs :

Numéro de projet	Titre du projet	Motifs
SUM_CDN24-0803	Réaménagement de l'intersection Somerled / Rosedale	Projet non-sélectionné en raison de limitations budgétaires.
SUM_CDN24-0804	Réaménagement géométrique de l'intersection Mackenzie / Lavoie	Projet non-sélectionné en raison de limitations budgétaires.
SUM_CDN24-0805	Réaménagement de l'intersection Lemieux / Dornal	Projet non-sélectionné en raison de limitations budgétaires.
SUM_CDN24-0806	Réaménagement géométrique de l'intersection Somerled/Doherty	Projet non-sélectionné en raison de limitations budgétaires.
SUM_CDN24-0807	Réaménagement de l'intersection Kensington / Biermans	Projet non-sélectionné en raison de limitations budgétaires.
SUM_CDN24-0902	Réaménagement de l'intersection Victoria et Fulton	Projet non-sélectionné en raison de limitations budgétaires.
SUM_CDN24-0905	Quai d'embarquement sur l'avenue Barclay vers l'avenue de Darlington	Projet non-sélectionné en raison de limitations budgétaires.
SUM_CDN24-0915	Aménagement d'un lien cyclable sur les rues Jean-Brillant et Louis-Collin	Projet non-sélectionné en raison de limitations budgétaires.
SUM_CDN24-0918	Aménagement d'un quai d'embarquement sur l'avenue Fielding vers l'avenue Walkley	Projet non-sélectionné en raison de limitations budgétaires.
SUM_CDN24-0926	Implantation d'un lien cyclable sur la rue Coronation, entre Côte-Saint-Luc et la rue Fielding	Projet non-sélectionné en raison de limitations budgétaires.
SUM_CDN24-0927	Mise à sens unique de l'avenue Bourret entre Clanranald et Décarie	Projet non-sélectionné en raison de limitations budgétaires.
SUM_CDN24-0939	Réaménagement de l'intersection de la rue Snowdon et l'avenue Clanranald	Projet non-sélectionné en raison de limitations budgétaires.
SUM_CDN24-0941	Réaménagement de l'avenue Coolbrook entre la rue Snowdon et le chemin Queen-Mary	Projet non-sélectionné en raison de limitations budgétaires.
SUM_CDN24-0942	Aménagrement d'un quai d'embarquement sur l'avenue Goyer vers l'avenue de Darlington	Projet non-sélectionné en raison de limitations budgétaires.

Numéro de projet	Titre du projet	Motifs
SUM_CDN24-0943	Étude de mobilité sur l'avenue Isabella en vue d'ajouter un aménagement cyclable	Projet non-sélectionné en raison de limitations budgétaires.
SUM_CDN24-0962	Aménagement d'un quai d'embarquement sur l'avenue Walkley vers le chemin Côte-Saint-Luc	Projet non-sélectionné en raison de limitations budgétaires.
SUM_CDN24-0971	Réaménagement de l'avenue Légaré	Projet non-sélectionné en raison de limitations budgétaires.
SUM_CDN24-0986	Réduction des limites de vitesse sur quatre artères principales du réseau routier supérieur de l'arrondissement de Côte-des-Neiges-Notre-Dame-de-Grâce : Jean-Talon, Côte-Saint-Luc, Saint-Jacques, le boulevard Décarie	Demande de projet non-conforme puisque visant le financement d'étude de circulation.

Activités subséquentes

Pour les projets dont les interventions sont localisées sur le Réseau artériel administratif de la Ville (RAAV) ou sur le Réseau cyclable, au plus tôt, votre arrondissement devra soumettre un dossier décisionnel à votre conseil afin que ce dernier adopte, en vertu du deuxième alinéa de l'article 85 de la Charte de la Ville de Montréal, une résolution visant à offrir vos services au conseil de la Ville en vue de la prise en charge de la réalisation des projets sélectionnés.

Ce dossier décisionnel devra notamment faire référence au numéro et au nom des projets sélectionnés ci-haut ainsi que préciser les informations suivantes, lorsqu'applicable :

- Le nombre de kilomètres de voie cyclable protégée ajoutés au réseau;
- Le nombre de kilomètres de voie cyclable non protégée ajoutés au réseau;
- Le nombre de SAS vélo ajoutés au réseau;
- Le nombre de kilomètres de rues réaménagés;
- Le nombre d'intersections sécurisées/réaménagées;
- Le nombre de m2 nouvellement verdis ou déminéralisés;
- Le nombre d'arbres ajoutés.

En contrepartie, un dossier décisionnel, préparé par le SUM, sera présenté au conseil de la Ville afin d'accepter l'offre de services de votre arrondissement.

Par la suite, pour l'ensemble des projets, nous vous rappelons que :

- La réalisation des projets doit être terminée d'ici la fin de l'année 2024;
- L'écart entre le montant de la dépense totale du projet et le budget estimé ne peut excéder 20% de ce dernier. À cet effet, un formulaire justificatif et explicatif devra être rempli par les personnes responsables en arrondissement;
- Les plans à 50% d'avancement doivent être envoyés au SUM pour commentaires;
- Les commentaires formulés par le SUM devront être intégrés aux projets;

- Advenant le refus d'appliquer un commentaire technique au projet émis par les équipes du SUM, l'arrondissement devra justifier l'exclusion de la recommandation technique;
- Le SUM se réserve le droit de retirer le financement du projet si une ou plusieurs exigences techniques émises par les équipes du SUM ne sont pas prises en compte.

Veuillez noter qu'un suivi de l'évolution des travaux sera effectué au courant de l'année.

Je vous prie de recevoir, Monsieur, mes meilleures salutations.


Le Directeur,


Hugues Bessette


Signature numérique de Hugues Bessette
Date : 2024.01.16 14:45:47 -05'00'


HB/tb

c. c. M. Pascal Trottier, chef de division - études techniques en arrondissement – arr. CDN-NDG
Mme Lucie Careau, directrice - Service de l'urbanisme et de la mobilité (SUM)
Mme Ève Leduc, cheffe de division – aménagement des rues – Direction des projets d'aménagement urbain - SUM
M. Damien Le Henanff, chef de division - administration et gestion de portefeuille - SUM

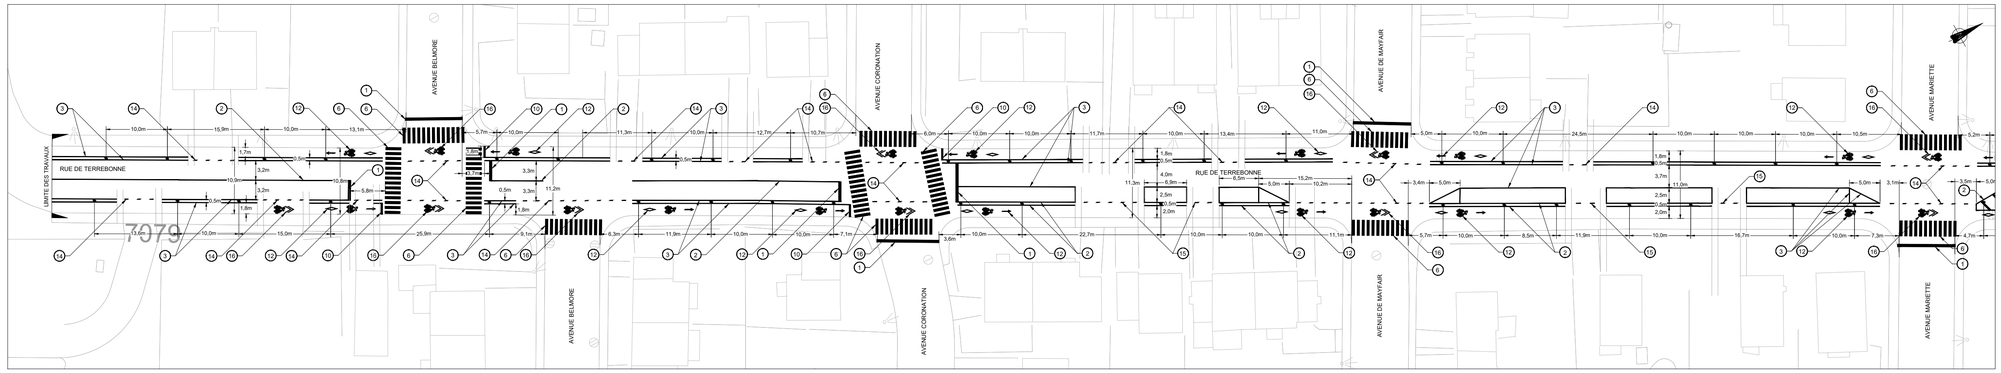

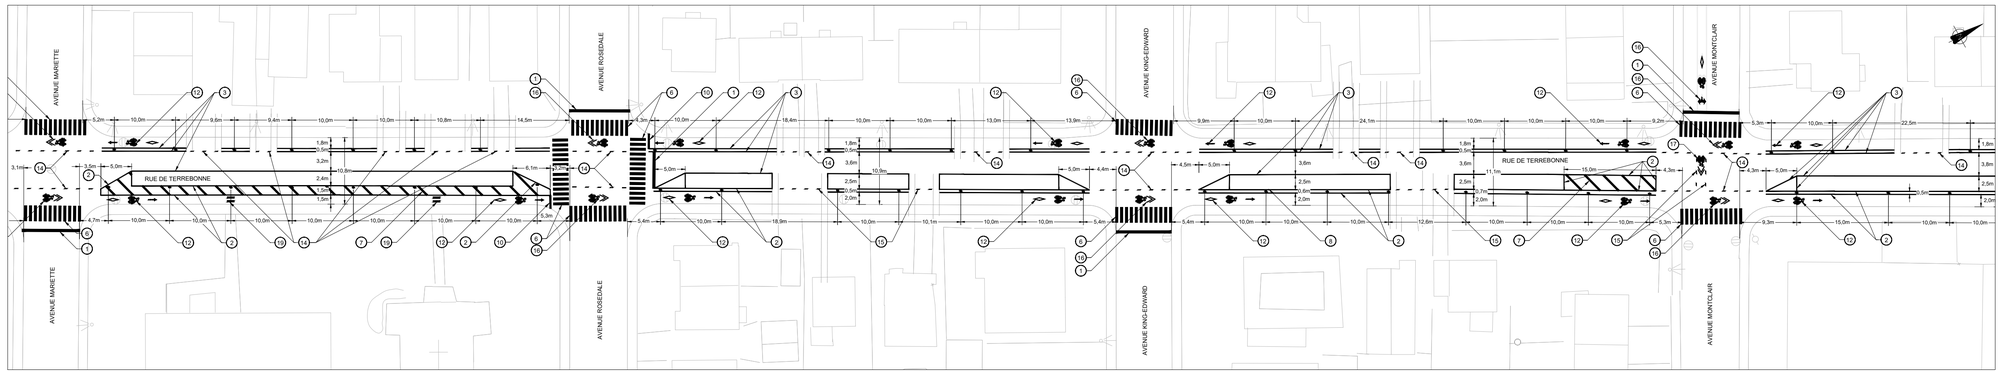

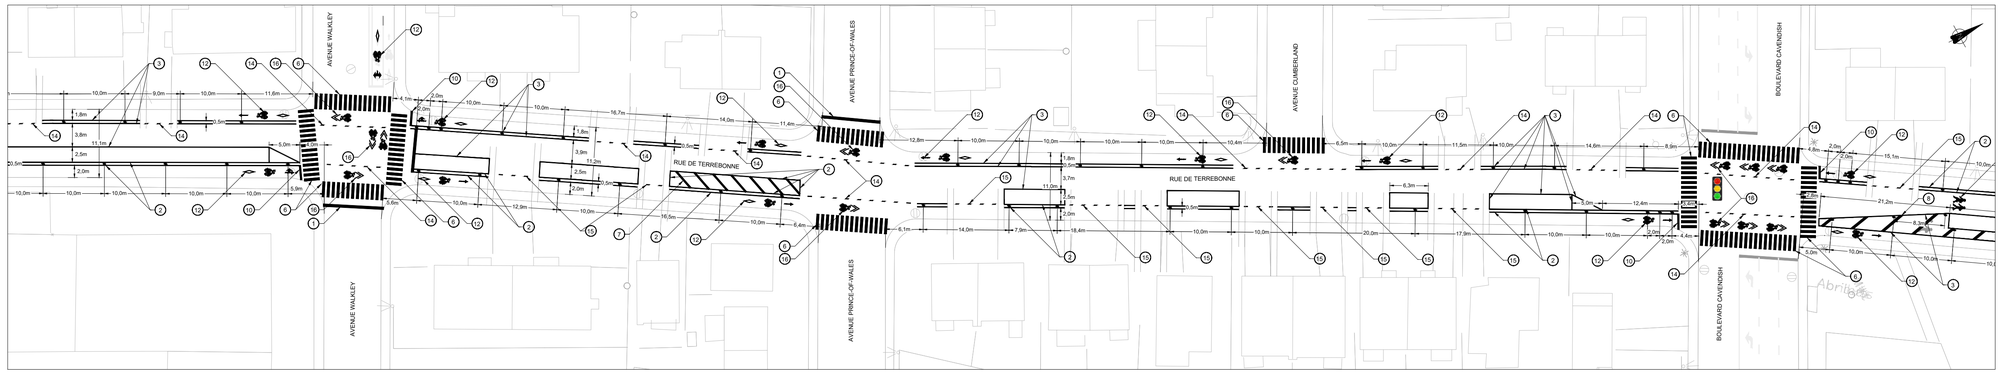

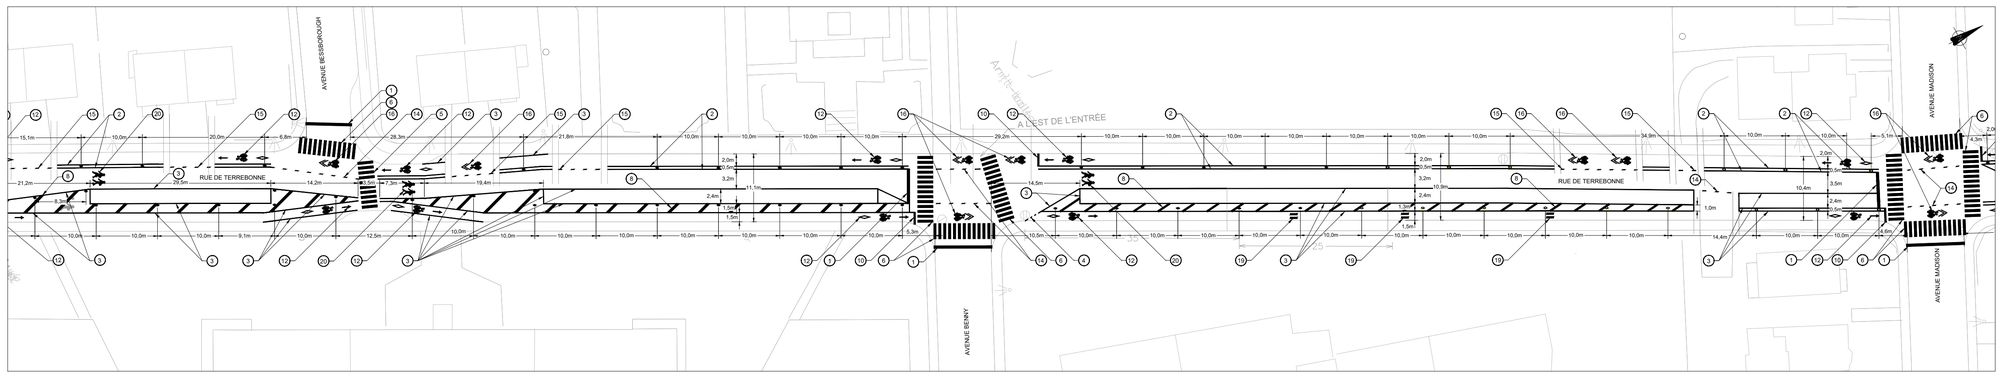

NOTE:

LES BOLLARDS DOIVENT ÊTRE INSTALLER À 0,25m DE LA LIGNE ENTRE LA ZONE TAMPON ET LA VOIE DE STATIONNEMENT OU DE CIRCULATION

Légende

IDENTIFICATION	DIMENSION	COULEUR	DESCRIPTION
0			MARQUAGE EXISTANT À EFFACER
1		BLANCHE	LIGNE D'ARRÊT 400mm DE LARGEUR
2		JAUNE	LIGNE AXIALE CONTINUE 120mm DE LARGEUR
3		BLANCHE	LIGNE DE DÉLIMITATION DE VOIES CONTINUE 120mm DE LARGEUR
4	1,0 1,0	BLANCHE	LIGNE DISCONTINUE EN BISEAU MARQUAGE DE MOYENNE DURÉE 120mm DE LARGEUR
5	0,4 0,4 2,5	JAUNE	BANDE DE PASSAGE 400mm DE LARGEUR
6	0,4 0,4 2,5	BLANCHE	
7	5,0 (S.I.C.)** 45°	JAUNE	HACHURES 400mm DE LARGEUR
8	5,0 (S.I.C.)** 45°	BLANCHE	
9		BLANCHE	FLÈCHES DE SÉLECTION DES VOIES COTÉES À PARTIR DE LA LIGNE D'ARRÊT (TYPE1)
10		BLANCHE	LIGNE D'ARRÊT 300mm DE LARGEUR
11	30°	BLANCHE	ZONE INTERDICTION D'ARRÊT MARQUAGE DE MOYENNE DURÉE 400mm DE LARGEUR
12		BLANCHE	CHEVRONS DE VOIE CYCLABLE BICYCLETTE DE VOIE CYCLABLE MACLE DE VOIE CYCLABLE MARQUAGE DE MOYENNE DURÉE
13		BLANCHE	SYMBOLE VOIE CYCLABLE SAS
14	1,0 1,5	BLANCHE	LIGNE DE PASSAGE POUR CYCLISTES 120mm DE LARGEUR
15	1,0 1,5	JAUNE	
16		BLANCHE	CHEVRON
17		JAUNE	
18	2,0	BLANCHE	PASSAGE POUR PERSONNES MARQUAGE DE MOYENNE DURÉE 100mm DE LARGEUR
19	0,3 0,3	JAUNE	BANDE DE PASSAGE POUR PERSONNES SUR LA VOIE CYCLABLE 300mm DE LARGEUR
20		BLANCHE	MARQUAGE ZONE SCOLAIRE

* LES COTES SONT EN MÈTRES
** SAUF INDICATION CONTRAIRE

Notes

Émission

N°	Date	Description	Prép. par	Resp. projet
0C	2024-05-30	ÉMISSION 100 %	E.C.	C.T.
0B	2024-04-23	ÉMISSION 70 %	E.C.	C.T.
0A	2024-03-08	ÉMISSION 30 %	E.C.	C.T.

FNX INNOV
433, rue Chabanel Ouest, 12e étage
Montréal (Québec)
Canada H2N 2J8
Tél. (514) 982-6001
Télé. (514) 982-6106
fnx-innov.com

Côte-des-Neiges
Notre-Dame-de-Grâce
Montréal

Arrondissement Côte-des-Neiges-Notre-Dame-de-Grâce
Division des études techniques
Direction des travaux publics
2140, avenue Madison, 3e étage, Montréal (Québec) H4B 2T4

Intervenants

Relevé au terrain: ---
Dessiné par: A. LÉVESQUE, tech. ---
Préparé par: É. CUSSON, ING., ENV SP ---
Vérifié par: C. TAILLÉE, ING., D.E.S.S. --

CES DOCUMENTS NE DOIVENT PAS ÊTRE UTILISÉS À DES FINS DE CONSTRUCTION OU DE FABRICATION

Sceau de l'ingénieur(e):

Original signé le:

Localisation:
Rue de Terrebonne
De l'avenue Belmore à l'avenue Girouard

Arrondissement(s): **Côte-des-Neiges-Notre-Dame-de-Grâce**


Nature des travaux:
PLANS DE MARQUAGE, SIGNALISATION ET FEUX RELATIVEMENT À L'IMPLANTATION DE LIENS CYCLABLES DANS CDN - NDG


Titre du plan:
PLANS DE MARQUAGE ET SIGNALISATION VERTICALE


(SI) DIMENSIONS EN MÈTRES, SAUF INDICATION CONTRAIRE


Échelle: 1 : 500
0 2,5 5,0 10,0 15,0 20,0 (mètres)

N° de soumission: **XXXXX**
N° de plan: **04**

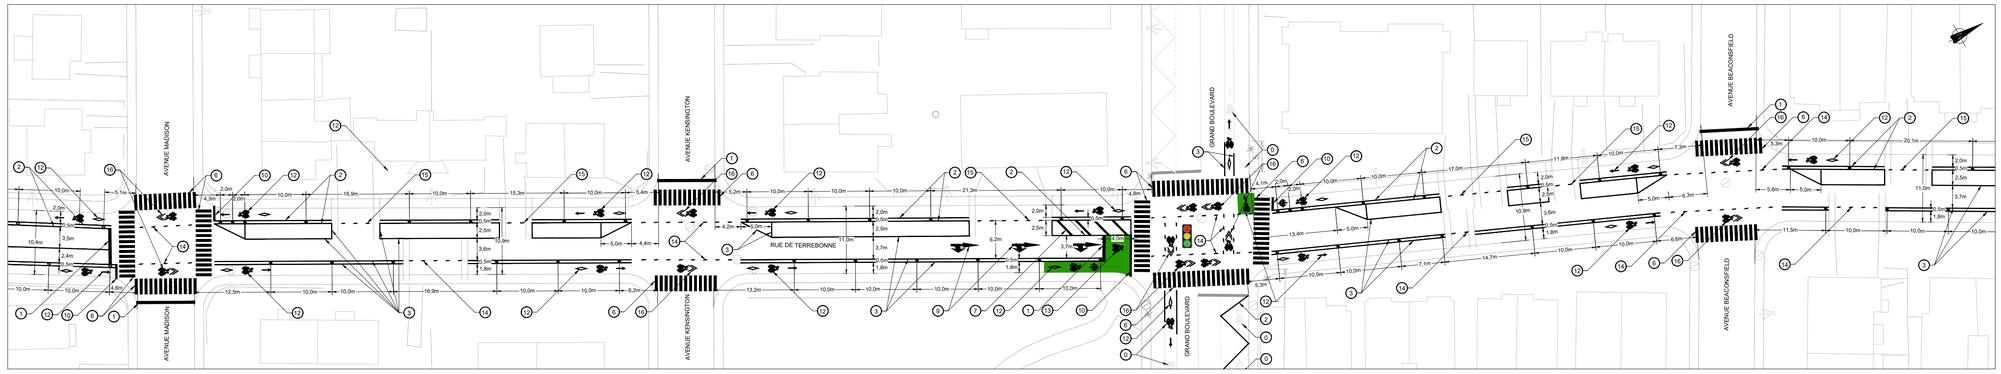

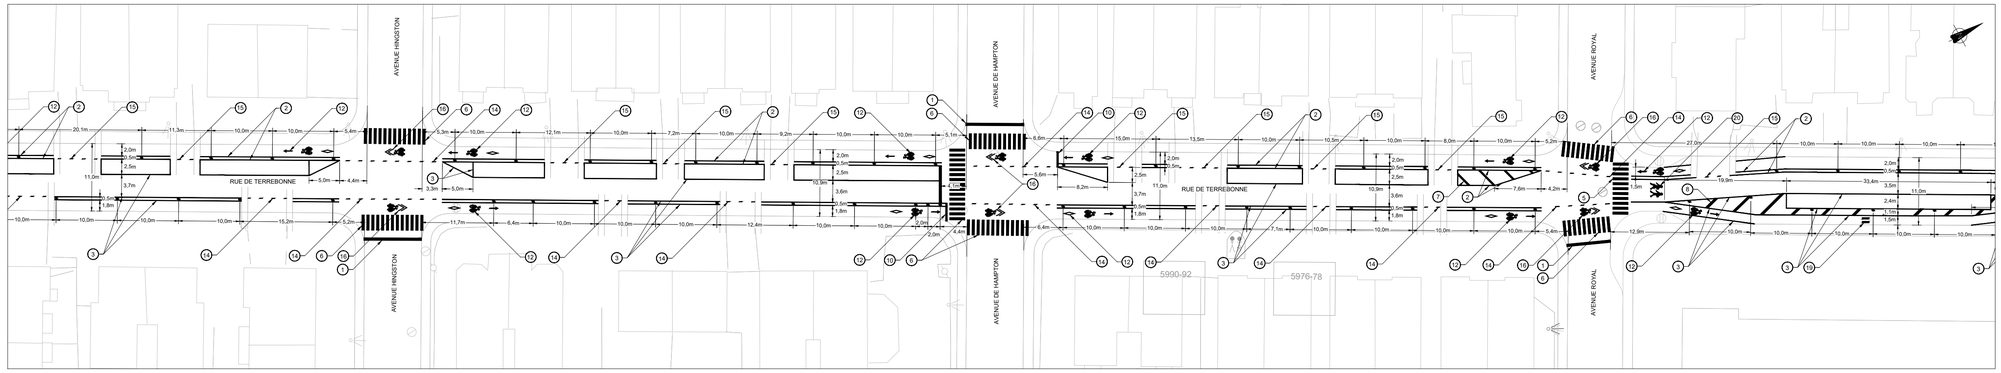

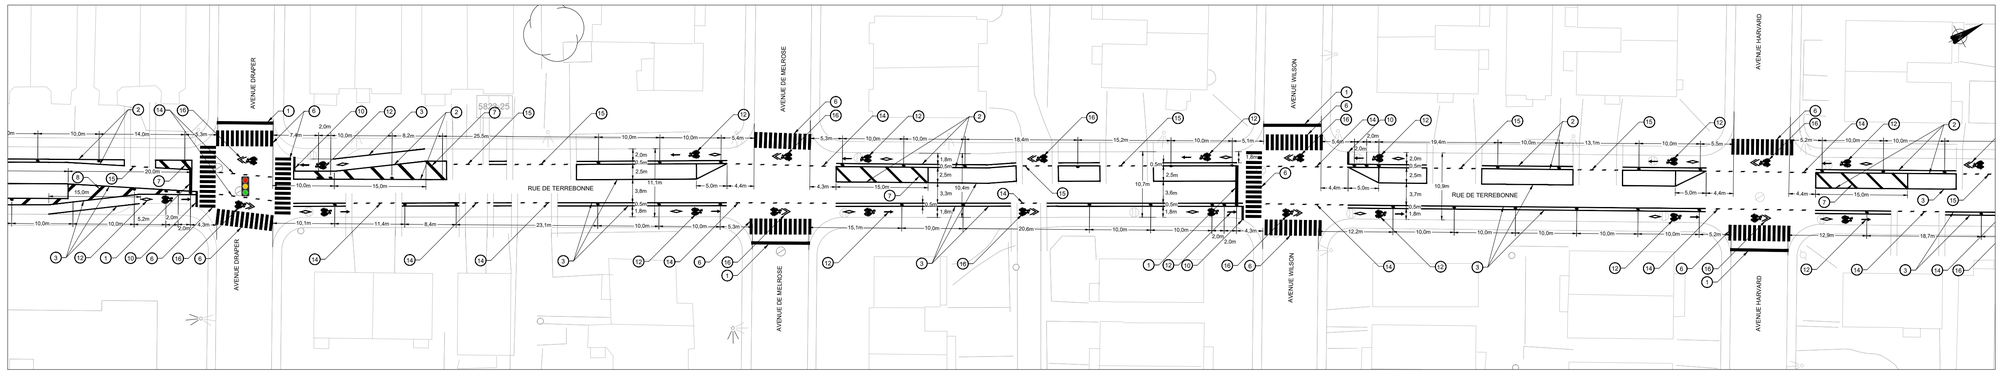

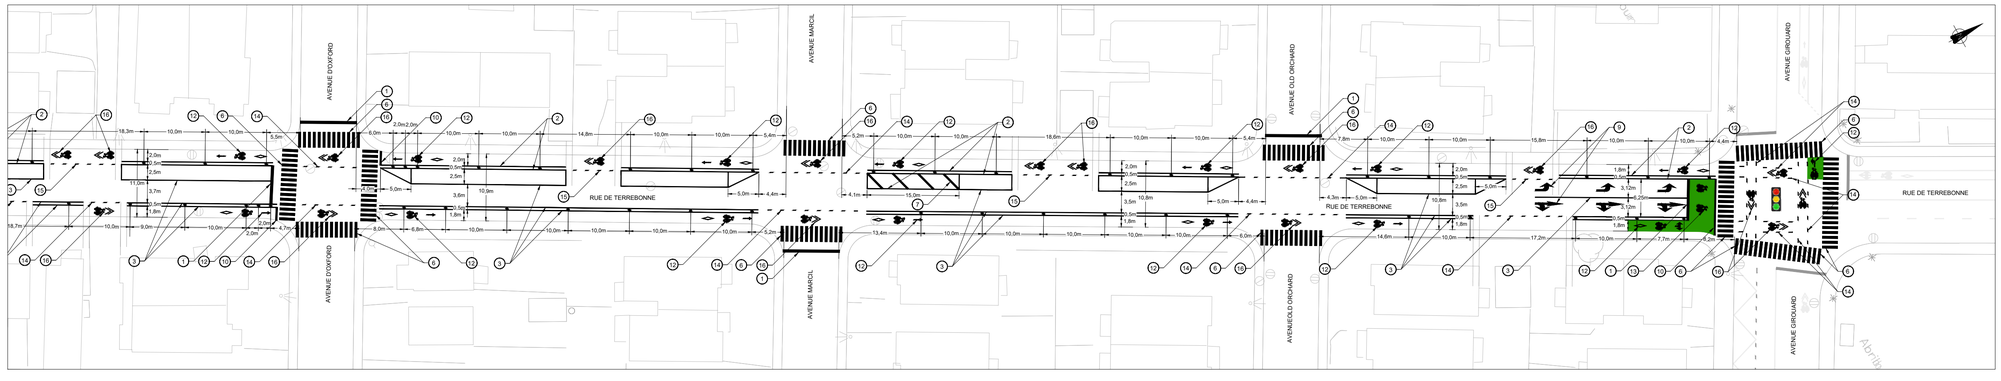

NOTE:

LES BOLLARDS DOIVENT ÊTRE INSTALLER À 0,25m DE LA LIGNE ENTRE LA ZONE TAMPON ET LA VOIE DE STATIONNEMENT OU DE CIRCULATION

Notes

Légende

IDENTIFICATION	DIMENSION	COULEUR	DESCRIPTION
0			MARQUAGE EXISTANT À EFFACER
1		BLANCHE	LIGNE D'ARRÊT 400mm DE LARGEUR
2		JAUNE	LIGNE AXIALE CONTINUE 120mm DE LARGEUR
3		BLANCHE	LIGNE DE DÉLIMITATION DE VOIES CONTINUE 120mm DE LARGEUR
4	1.0 1.0	BLANCHE	LIGNE DISCONTINUE EN BISEAU MARQUAGE DE MOYENNE DURÉE 120mm DE LARGEUR
5	0.4 0.4 2.5	JAUNE	BANDE DE PASSAGE 400mm DE LARGEUR
6	0.4 0.4 2.5	BLANCHE	
7	5.0 (S.I.C.)** 45°	JAUNE	HACHURES 400mm DE LARGEUR
8	5.0 (S.I.C.)** 45°	BLANCHE	
9		BLANCHE	FLÈCHES DE SÉLECTION DES VOIES COTÉES À PARTIR DE LA LIGNE D'ARRÊT (TYPE1)
10		BLANCHE	LIGNE D'ARRÊT 300mm DE LARGEUR
11	45°	BLANCHE	ZONE INTERDICTION D'ARRÊT MARQUAGE DE MOYENNE DURÉE 400mm DE LARGEUR
12		BLANCHE	CHEVRONS DE VOIE CYCLABLE BICYCLETTE DE VOIE CYCLABLE MACLE DE VOIE CYCLABLE MARQUAGE DE MOYENNE DURÉE
13		BLANCHE	SYMBOLE VOIE CYCLABLE SAS
14	1.0 1.5	BLANCHE	LIGNE DE PASSAGE POUR CYCLISTES 120mm DE LARGEUR
15	1.0 1.5	JAUNE	
16		BLANCHE	CHEVRON
17		JAUNE	
18	2.5	BLANCHE	PASSAGE POUR PERSONNES MARQUAGE DE MOYENNE DURÉE 100mm DE LARGEUR
19	0.3 0.3 3.2	JAUNE	BANDE DE PASSAGE POUR PERSONNES SUR LA VOIE CYCLABLE 300mm DE LARGEUR
20		BLANCHE	MARQUAGE ZONE SCOLAIRE

* LES COTES SONT EN MÈTRES
** SAUF INDICATION CONTRAIRE

Émission

N°	Date	Description	Prép. par	Resp. projet
0C	2024-05-30	ÉMISSION 100 %	E.C.	C.T.
0B	2024-04-23	ÉMISSION 70 %	E.C.	C.T.
0A	2024-03-08	ÉMISSION 30 %	E.C.	C.T.

FNX INNOV
433, rue Chabanel Ouest, 12e étage
Montréal (Québec)
Canada H2N 2J8
Tél. (514) 982-6001
Télé. (514) 982-6106
fnx-innov.com

Côte-des-Neiges
Notre-Dame-de-Grâce
Montréal

Arrondissement Côte-des-Neiges-Notre-Dame-de-Grâce
Division des études techniques
Direction des travaux publics
2140, avenue Madison, 3e étage, Montréal (Québec) H4B 2T4

Intervenants

Relevé au terrain: ---
Dessiné par: A. LÉVESQUE, tech. ---
Préparé par: É. CUSSON, ING., ENV SP ---
Vérifié par: C. TAILLÉE, ING., D.E.S.S. --

CES DOCUMENTS NE DOIVENT PAS ÊTRE UTILISÉS À DES FINS DE CONSTRUCTION OU DE FABRICATION

Sceau de l'ingénieur(e):

Original signé le:

Localisation:
Rue de Terrebonne
De l'avenue Belmore à l'avenue Girouard

Arrondissement(s): **Côte-des-Neiges-Notre-Dame-de-Grâce**


Nature des travaux:
PLANS DE MARQUAGE, SIGNALISATION ET FEUX RELATIVEMENT À L'IMPLANTATION DE LIENS CYCLABLES DANS CDN - NDG


Titre du plan:
PLANS DE MARQUAGE ET SIGNALISATION VERTICALE


(SI) DIMENSIONS EN MÈTRES, SAUF INDICATION CONTRAIRE


Échelle: 1 : 500
0 2,5 5,0 10,0 15,0 20,0 (mètres)

N° de soumission: **XXXXX**
N° de plan: **05**

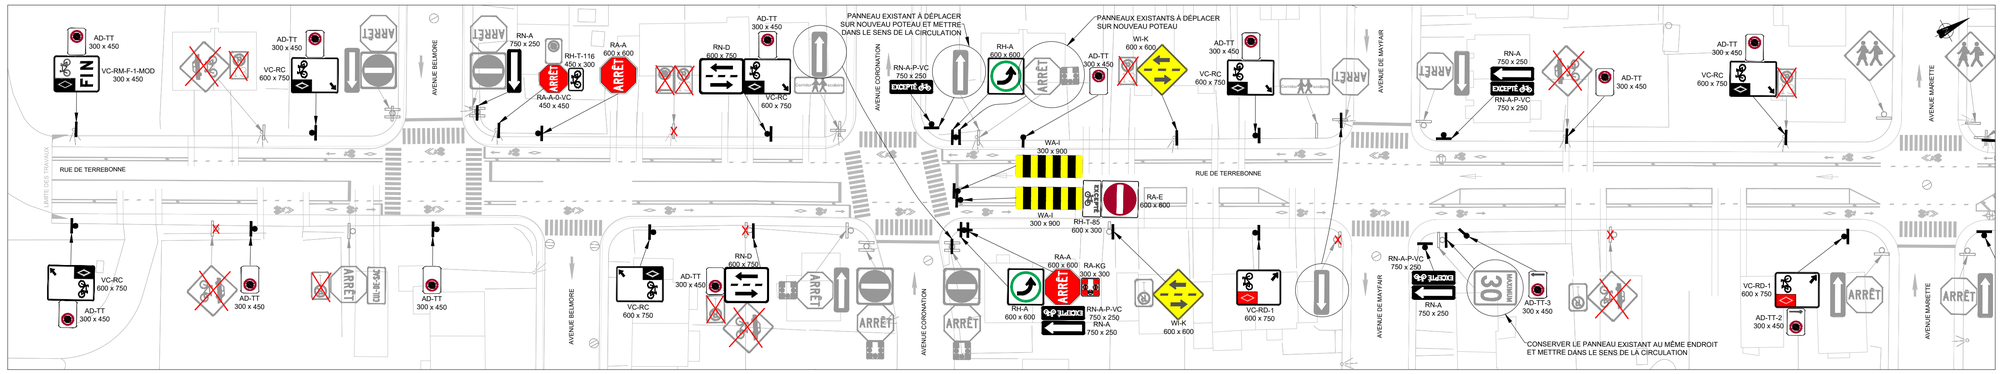

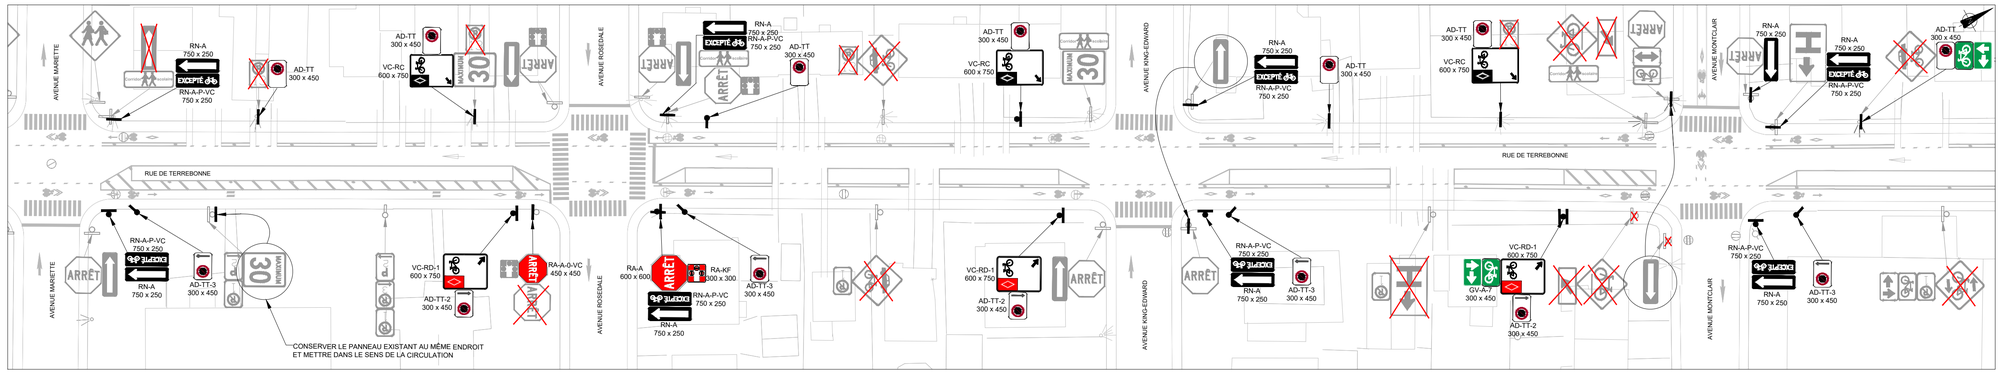

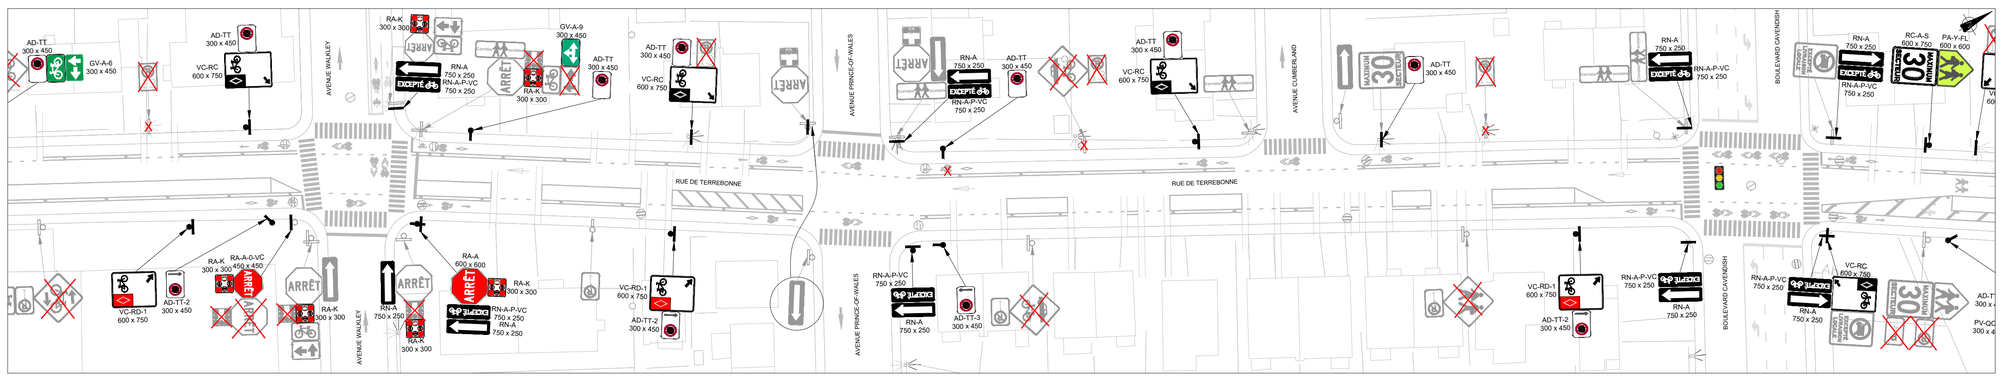

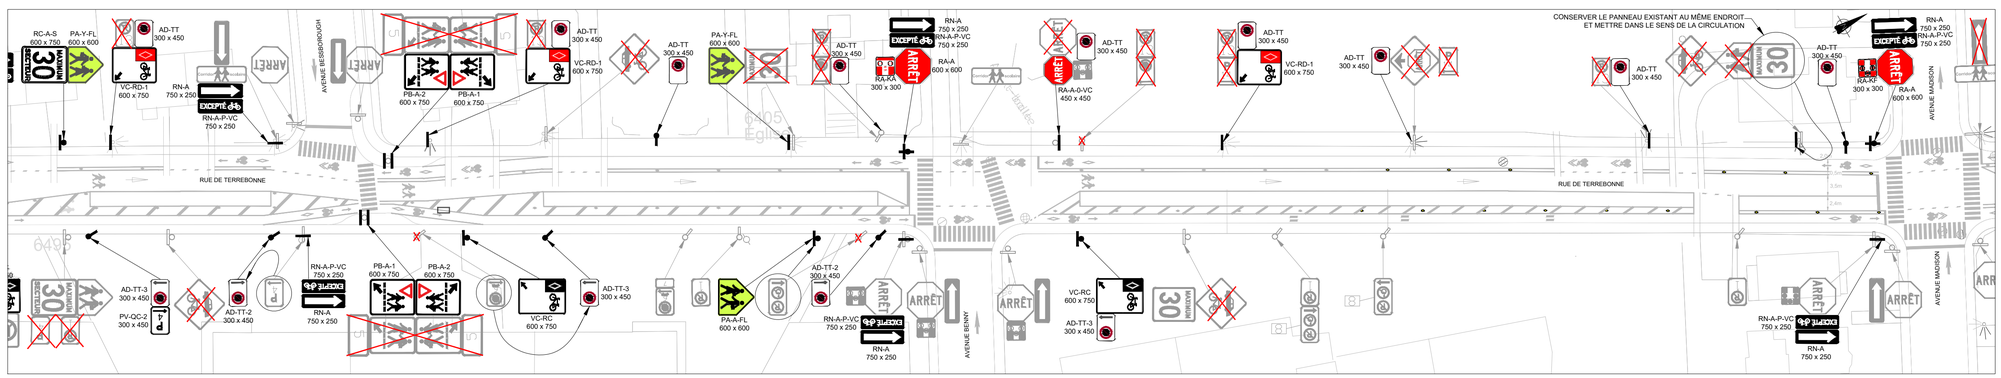

Légende

EXISTANTS	PROPOSÉS
PANNEAU EXISTANT	PANNEAU À INSTALLER
PANNEAU EXISTANT À ENLEVER	PANNEAU ET SUPPORT À INSTALLER
PANNEAU EXISTANT À RÉCUPÉRER ET DÉPLACER	PANNEAU À INSTALLER SUR SUPPORT EXISTANT
PANNEAU ET SUPPORT EXISTANT	
POTENCE EXISTANT	NOUVELLE POTENCE

Notes

id	text
1	12h30 - 14h30 MERCREDI 1 AVRIL AU 1 DÉC
2	15 min. 9h-15h MAR. ET MER.
3	8H - 17h LUN AU SAM
4	15 min 7h-9h30 15h - 18h LUN À VEN
5	PRIORITÉ AUX PIÉTONS
6	8h - 16h LUN À VEN SEPT À JUIN EXCEPTÉ
7	EXCEPTÉ PÉRIODE INTERDITE
8	RÉSERVÉ DÉBARCADÈRE
9	8h - 17h JOURS D'ÉCOLE
10	10h - 12h MERCREDI 1 AVRIL AU 1 DÉC
11	15 min DÉBARCADÈRE 7h - 18h LUN À VEN
12	10h - 12h LUNDI 1 AVRIL AU 1 DÉC
13	12h30 - 14h30 LUNDI 1 AVRIL AU 1 DÉC
14	15 min 7h - 9h 14h - 16h LUN À VEN SEPT À JUIN

AUCUN PANNEAU OU DISPOSITIF DE SIGNALISATION NE DOIT ÊTRE INSTALLÉ AU DOS DU PANNEAU ARRÊT, ET CE POUR ÉVITER QUE LA FORME SOIT DIFFICILEMENT IDENTIFIABLE.

Émission

N°	Date	Description	Prép. par	Resp. projet
0C	2024-05-30	ÉMISSION 100 %	E.C.	C.T.
0B	2024-04-23	ÉMISSION 70 %	E.C.	C.T.
0A	2024-03-08	ÉMISSION 30 %	E.C.	C.T.

FNX INNOV
433, rue Chabanel Ouest, 12e étage
Montréal (Québec)
Canada H2N 2J8
Tél. (514) 982-6001
Télé. (514) 982-6106
fnx-innov.com

Côte-des-Neiges
Notre-Dame-de-Grâce
Montréal

Arrondissement Côte-des-Neiges-Notre-Dame-de-Grâce
Division des études techniques
Direction des travaux publics
2140, avenue Madison, 3e étage, Montréal (Québec) H4B 2T4

Intervenants

Relevé au terrain:	---
Dessiné par: A. LÉVESQUE, tech.	---
Préparé par: É. CUSSON, ING., ENV SP	---
Vérifié par: C. TAILLÉE, ING., D.E.S.S.	--

CES DOCUMENTS NE DOIVENT PAS ÊTRE UTILISÉS À DES FINS DE CONSTRUCTION OU DE FABRICATION

Sceau de l'ingénieur(e):

Original signé le:

Localisation:
Rue de Terrebonne
De l'avenue Belmore à l'avenue Girouard

Arrondissement(s): **Côte-des-Neiges-Notre-Dame-de-Grâce**

Nature des travaux:
PLANS DE MARQUAGE, SIGNALISATION ET FEUX
RELATIVEMENT À L'IMPLANTATION DE LIENS
CYCLABLES DANS CDN - NDG


Titre du plan:
PLANS DE SIGNALISATION VERTICALE


(SI) DIMENSIONS EN MÈTRES, SAUF INDICATION CONTRAIRE


Échelle:
1 : 500
0 2,5 5,0 10,0 15,0 20,0 (mètres)


N° de soumission:
XXXXX

N° de plan:
06

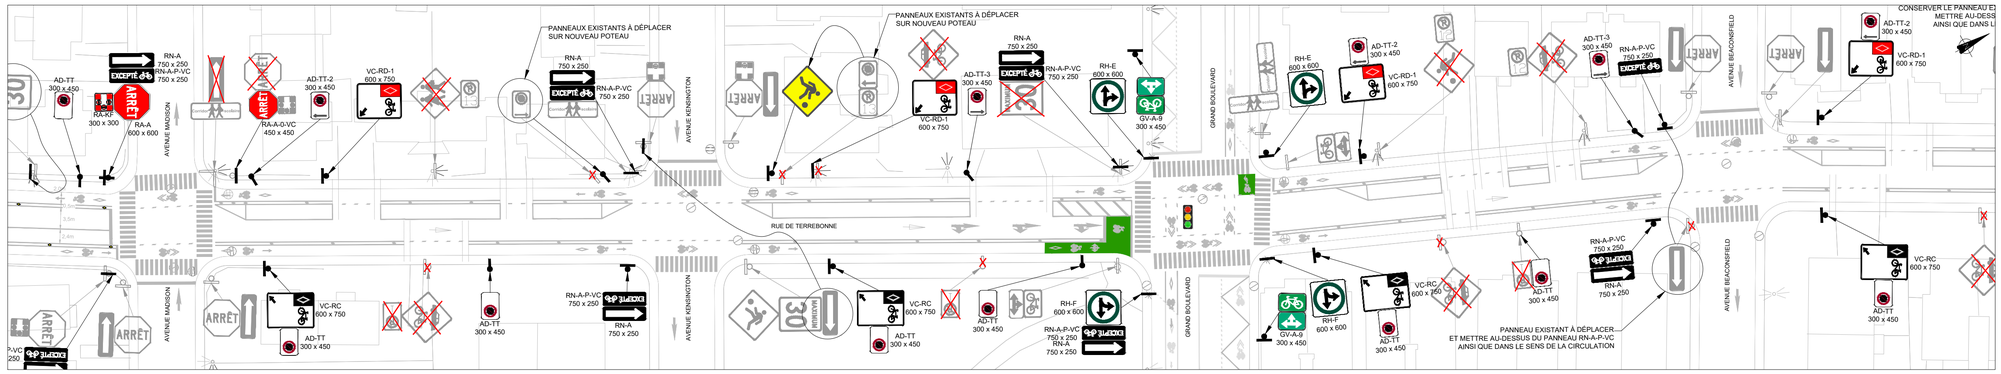

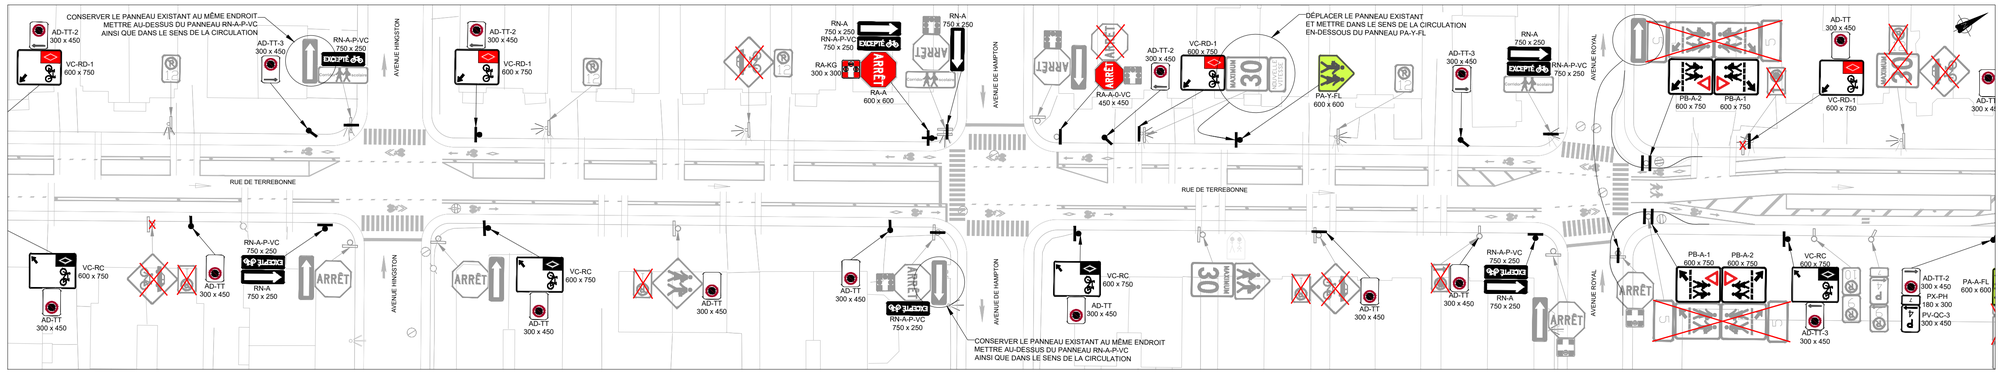

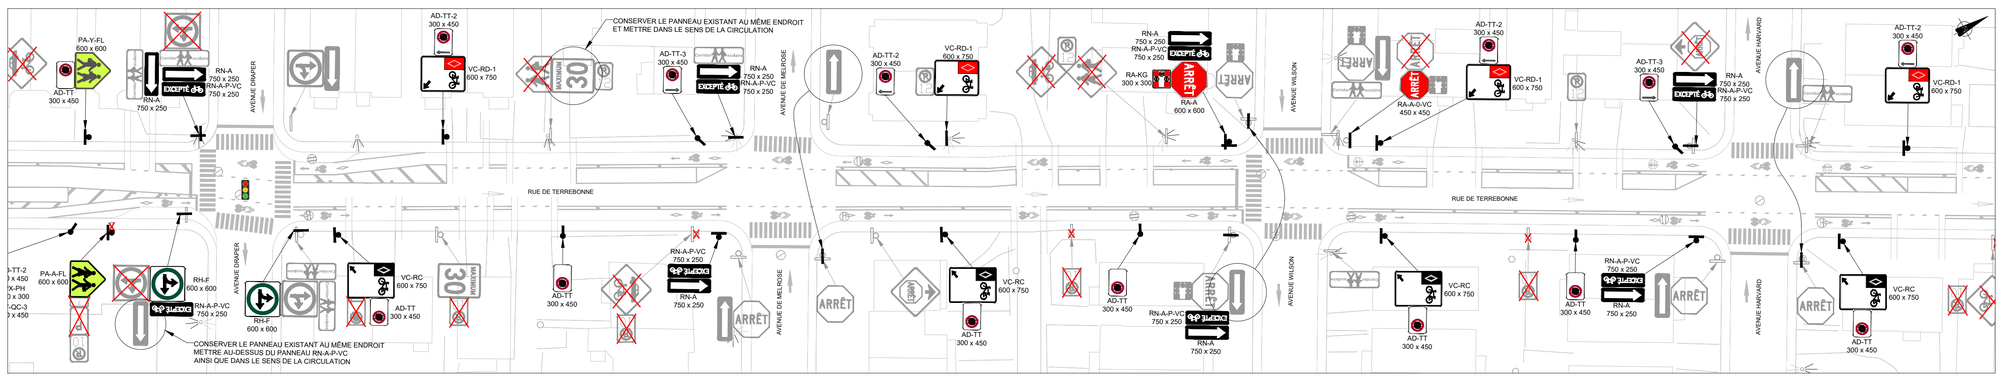

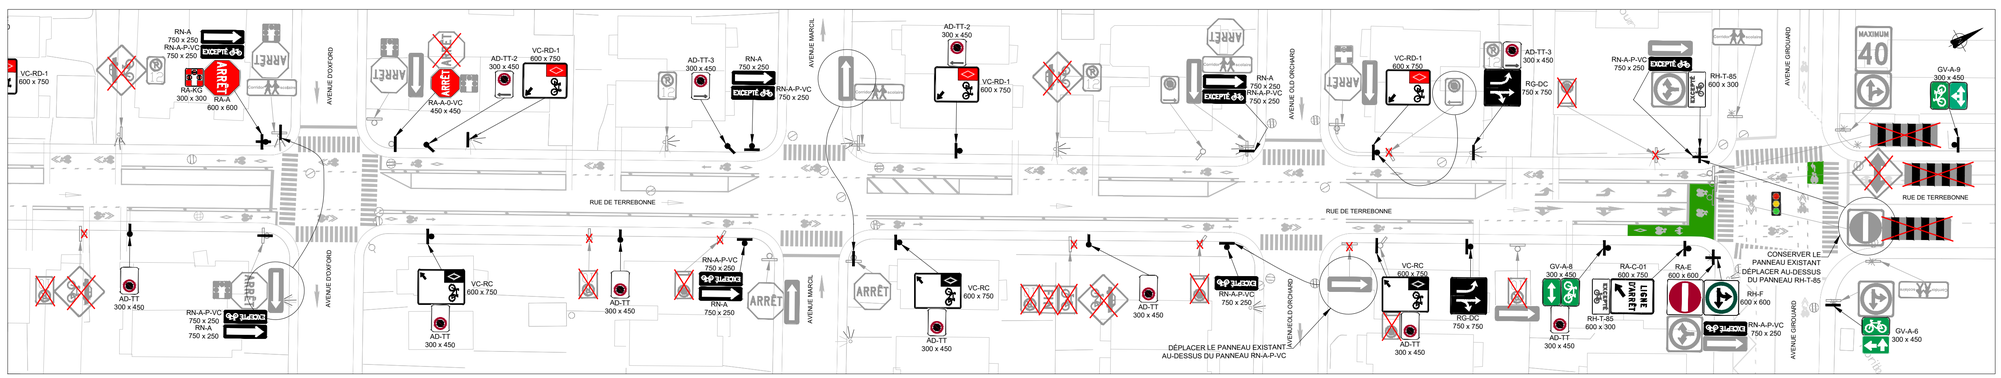

Légende

EXISTANTS	PROPOSÉS
PANNEAU EXISTANT	PANNEAU À INSTALLER
PANNEAU EXISTANT À ENLEVER	PANNEAU ET SUPPORT À INSTALLER
PANNEAU EXISTANT À RÉCUPÉRER ET DÉPLACER	PANNEAU À INSTALLER SUR SUPPORT EXISTANT
PANNEAU ET SUPPORT EXISTANT	
POTENCE EXISTANT	NOUVELLE POTENCE

Notes

id	text
1	12h30 - 14h30 MERCREDI 1 AVRIL AU 1 DÉC
2	15 min. 9h-15h MAR. ET MER.
3	8H - 17h LUN AU SAM
4	15 min 7h-9h30 15h - 18h LUN À VEN
5	PRIORITÉ AUX PIÉTONS
6	8h - 16h LUN À VEN SEPT À JUIN EXCEPTÉ
7	EXCEPTÉ PÉRIODE INTERDITE
8	RÉSERVÉ DÉBARCADÈRE
9	8h - 17h JOURS D'ÉCOLE
10	10h - 12h MERCREDI 1 AVRIL AU 1 DÉC
11	15 min DÉBARCADÈRE 7h - 18h LUN À VEN
12	10h - 12h LUNDI 1 AVRIL AU 1 DÉC
13	12h30 - 14h30 LUNDI 1 AVRIL AU 1 DÉC
14	15 min 7h - 9h 14h - 16h LUN À VEN SEPT À JUIN

AUCUN PANNEAU OU DISPOSITIF DE SIGNALISATION NE DOIT ÊTRE INSTALLÉ AU DOS DU PANNEAU ARRÊT, ET CE POUR ÉVITER QUE LA FORME SOIT DIFFICILEMENT IDENTIFIABLE.

Émission

0C	2024-05-30	ÉMISSION 100 %	E.C.	C.T.
0B	2024-04-23	ÉMISSION 70 %	E.C.	C.T.
0A	2024-03-08	ÉMISSION 30 %	E.C.	C.T.
N°	Date	Description	Prép. par	Resp. projet

FNX INNOV
433, rue Chabanel Ouest, 12e étage
Montréal (Québec)
Canada H2N 2J8
Tél. (514) 982-6001
Télé. (514) 982-6106
fnx-innov.com

Côte-des-Neiges
Notre-Dame-de-Grâce
Montréal

Arrondissement Côte-des-Neiges-Notre-Dame-de-Grâce
Division des études techniques
Direction des travaux publics
2140, avenue Madison, 3e étage, Montréal (Québec) H4B 2T4

Intervenants

Relevé au terrain: ---
Dessiné par: A. LÉVESQUE, tech. ---
Préparé par: É. CUSSON, ING., ENV SP ---
Vérifié par: C. TAILLÉE, ING., D.E.S.S. --

CES DOCUMENTS NE DOIVENT PAS ÊTRE UTILISÉS À DES FINS DE CONSTRUCTION OU DE FABRICATION

Sceau de l'ingénieur(e):

Original signé le:

Localisation: Rue de Terrebonne
De l'avenue Belmore à l'avenue Girouard

Arrondissement(s): **Côte-des-Neiges-Notre-Dame-de-Grâce**

Nature des travaux:
PLANS DE MARQUAGE, SIGNALISATION ET FEUX RELATIVEMENT À L'IMPLANTATION DE LIENS CYCLABLES DANS CDN - NDG

Titre du plan:

PLANS DE SIGNALISATION VERTICALE

(SI) DIMENSIONS EN MÈTRES, SAUF INDICATION CONTRAIRE

Échelle: 1 : 500

0 2,5 5,0 10,0 15,0 20,0 (mètres)

N° de soumission: **XXXXX**

N° de plan: **07**



OCA24 XXXXXX.doc

Côte-des-Neiges
Notre-Dame-de-Grâce
Montréal

RÈGLEMENT SUR LA CIRCULATION ET LE STATIONNEMENT
(R.R.V.M., chapitre C-4.1, article 3, paragraphe 3º)

Ordonnance numéro OCA24 XXXXX (C-4.1) relative à la mise à sens unique de la rue Terrebonne en vue d'ajouter un aménagement cyclable protégé entre les avenues Saint-Ignatius et l'avenue Girouard.

À la séance ordinaire du 3 juin 2024, le conseil d'arrondissement de Côte-des-Neiges—Notre-Dame-de-Grâce décrète :

-Édicter une ordonnance relative à la mise à sens unique de la rue Terrebonne en vue d'ajouter un aménagement cyclable protégé entre les avenues Saint-Ignatius et l'avenue Girouard

- Conserver toute autre réglementation en vigueur

GDD 1246880006

_____

ADOPTÉ PAR LE CONSEIL D'ARRONDISSEMENT DE CÔTE-DES-NEIGES—NOTRE-DAME-DE-GRÂCE LORS DE SA SÉANCE ORDINAIRE TENUE LE 3 JUIN 2024

_____
La mairesse d'arrondissement,
Gracia Kasoki Katahwa

_____
La secrétaire d'arrondissement,
Geneviève Reeves, avocate